




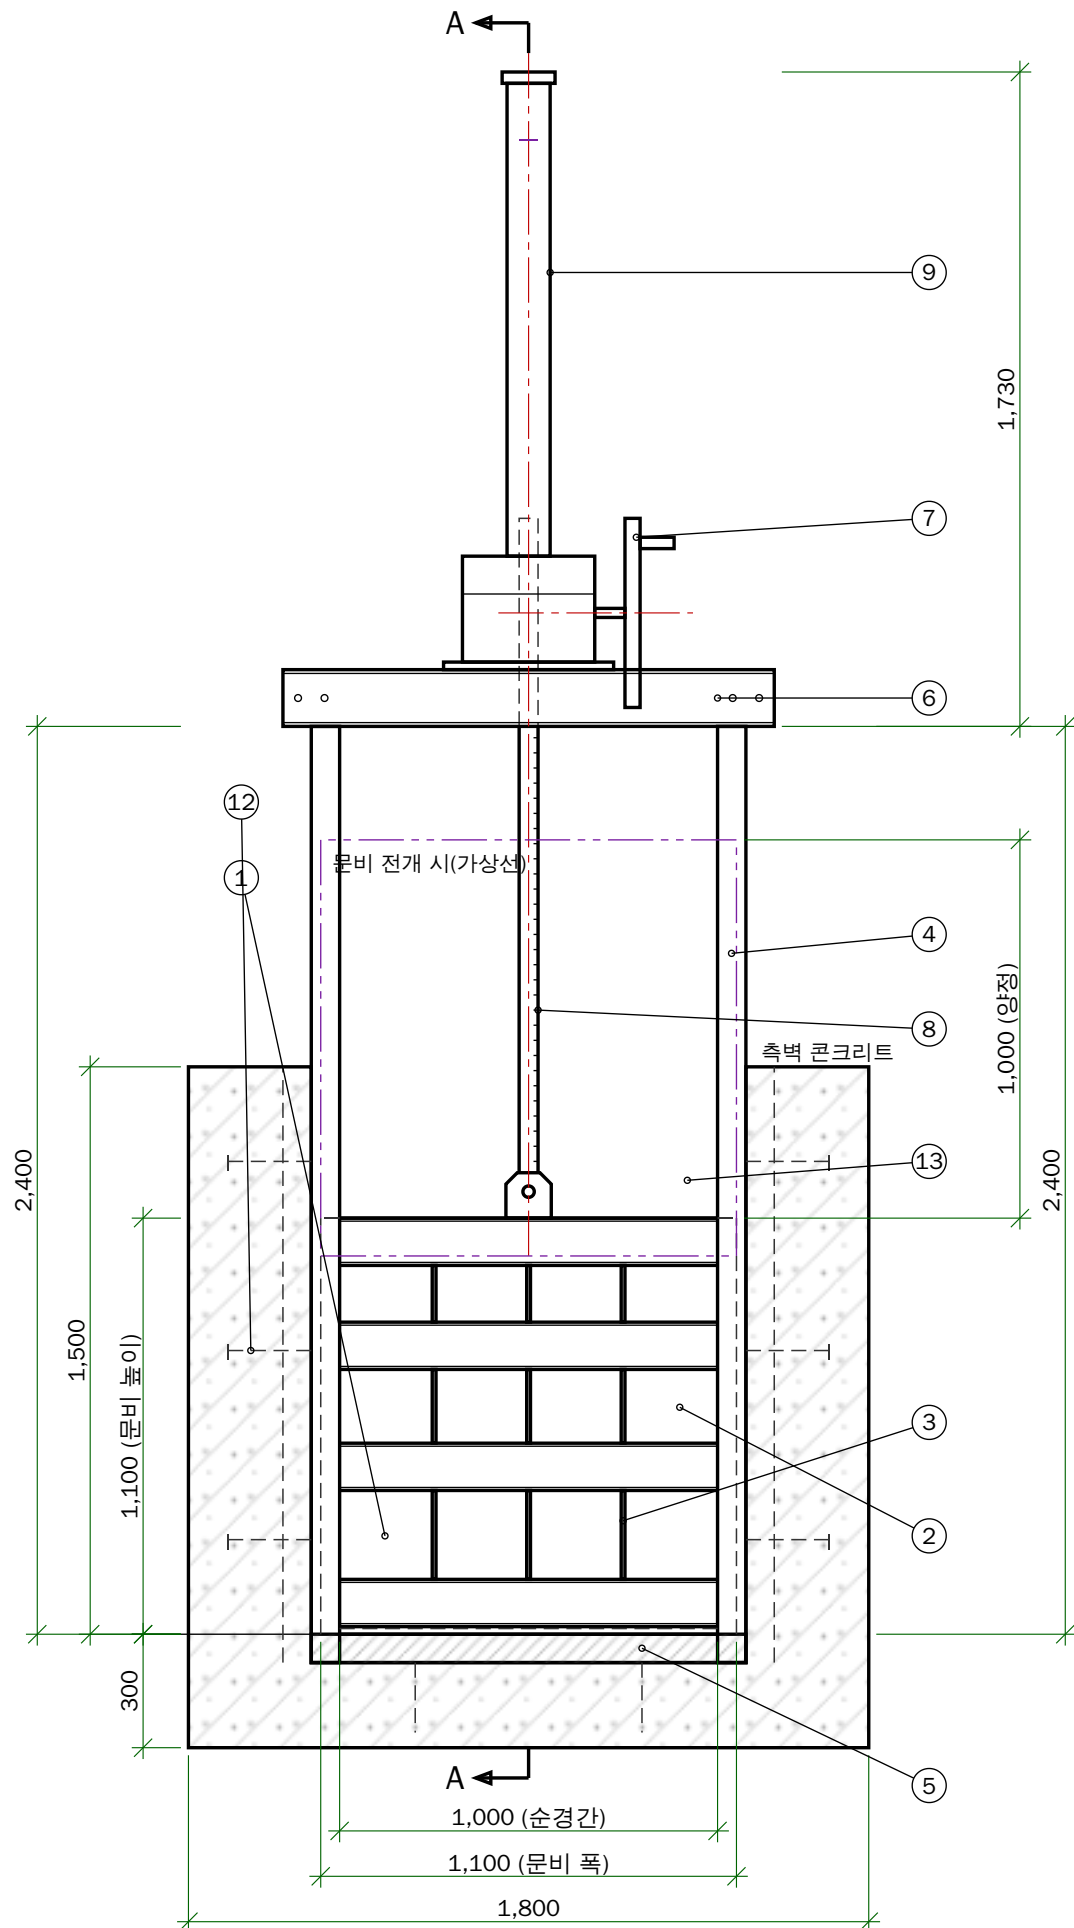

정면도 (하류측에서 봄)
S=1:20

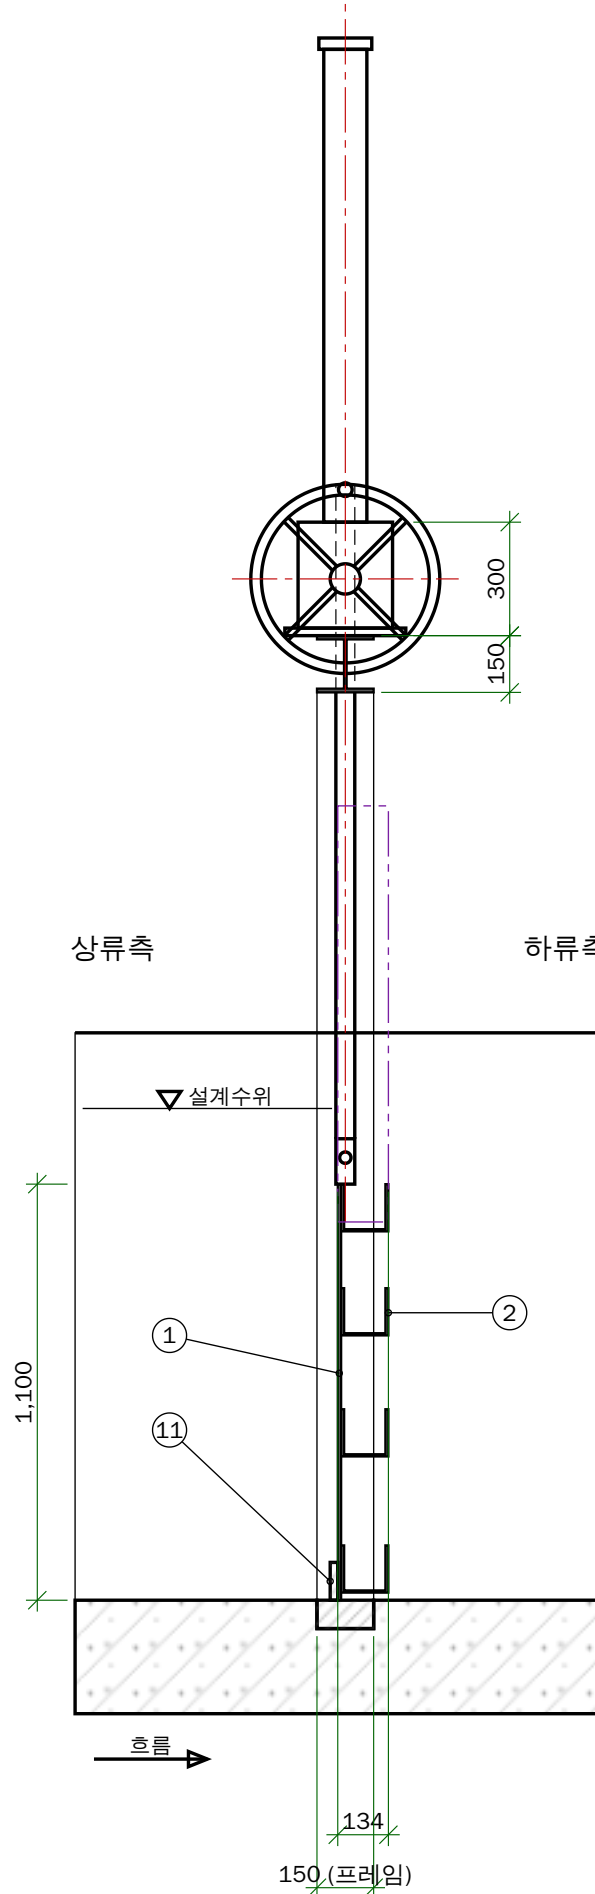

단면도 A-A
S=1:20

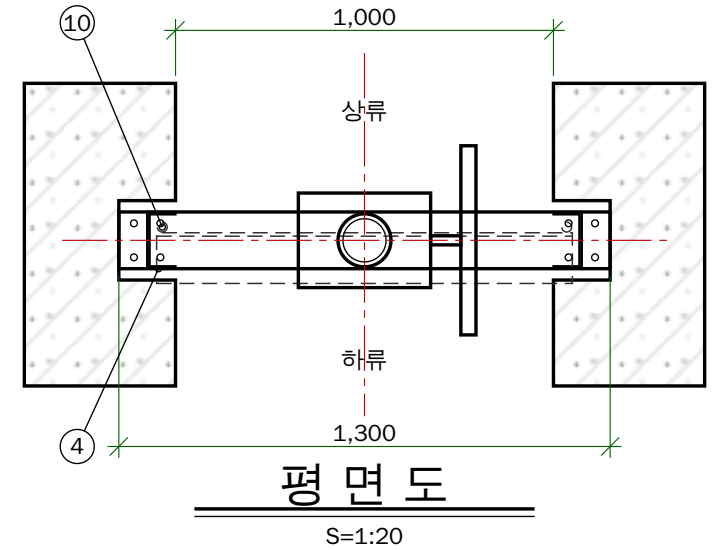

재료표

품번	품명	규격	재질	수량
1	스킨플레이트	PL 9×1,100×1,100	SS275	1
2	수평 주형	C-125×65×6 L=1,100	SS275	4
3	수직 보강재	FB 75×9	SS275	9
4	가이드 프레임	C-150×75×6.5 L=2,475	SS275	2
5	실(Sill) 빔	C-150×75×6.5 L=1,150	SS275	1
6	상부 빔(권양대)	H-150×150×7×10 L=1,300	SS275	1
7	랙식 개폐기(수동)	핸들 Ø500, 2.0 ton	조립품	1
8	랙 바	□50×50 L=1,800	SM45C	1
9	랙 커버 파이프	Ø114.3×4.5 L=1,250	STS304	1
10	측부 수밀고무	P형 Ø26	CR	2
11	하부 수밀고무	평형 20×100	CR	1
12	앵커볼트	M16×200	SS275(용융아연)	16
13	연결 러그·핀	PL 16, 핀 Ø30	SS275/STS304	1조

주 기

- 본 도면은 랙형 일체식 문비(수동 랙식 개폐기 일체형 수문)의 일반 참고도이며, 제작 전 현장 여건·설계수압에 따라 구조 검토 후 치수를 확정할 것.
- 치수 단위: mm
- 설계 조건(가정): 순경간 1,000, 문비 1,100×1,100, 양정 1,000, 설계수심 1.5 m
- 강재는 KS D 3503 SS275, 용접은 연속 필릿 용접(각장 6mm 이상)으로 한다.
- 도장: 무기질 아연말 하도 + 에폭시 중·상도(총 건조도막 250 μ m 이상)
- 가이드 프레임·실 빔은 1차 콘크리트 블록아웃 후 수직·수평을 맞추고 무수축 몰탈(2차 콘크리트)로 충전한다.
- 수밀고무는 CR(클로로프렌) 재질로 하며, 볼트 체결 후 누수 시험 실시.

도면명

랙형 일체식 문비 일반도

공사명

축척 1:20 (A3)

도면번호 G-001

작성일 2026. 10. 06

단위 mm

비고 참고도